

Compliance Notes:

The buildings must comply with Australian Standard AS 1428.1 - 'Design for Access and Mobility and Disability (Access to Premises - Buildings) Standards 2010

- Ensure an accessway is provided to a building required to be accessible from an existing building that is required to be accessible and from the main points of a pedestrian entry at the allotment boundary in accordance with Australian Standard AS 1428.1 - 'Design for Access and Mobility and Disability (Access to Premises - Buildings) Standards 2010.

- Bushfire Construction Requirements

The buildings must comply with the requirements of 'Planning for Bush Fire Protection 2019' prepared by Planning NSW 2573 and Australian Standard AS 3959 - 2018 'Construction of Buildings in Bush Fire Prone Areas'.

1. That the site where not built upon shall have the vegetation reduced where necessary to satisfy the requirements of 'Planning for Bush Fire Protection 2019 and the NSW Rural Fire Service document "Standards for Asset Protection Zones" for an inner protection area of an asset protection zone and this area shall be maintained at this vegetation level for the lifetime of the development as follows;

- To the north and west from Amenities Block 1 for a distance of 45 metres;

- To the east and south from Amenities Block 1 for a distance of 30 metres; and

- From Amenities Block 2 in each direction for a distance of 37 metres.

3. That the Amenities Blocks should be designed and constructed to the requirements of AS 3959-2018 and must be constructed to comply with section 3 Construction General and section 7 BAL 29 of such standard apart from as varied to comply with section 7.5.2 Additional Construction Requirements of Planning for Bushfire Protection 2019.

4. That if the supply of gas to buildings is undertaken it shall be installed and maintained in accordance with AS 1596-2002 and requirements of relevant authorities.



Grant Durrington
Accredited Certifier
2573

External Colours:

- Wall Sheeting = Shale Grey
- Windows = Shale Grey
- Downpipes = Shale Grey
- Roof Sheeting/Gutters/Flashings = Woodland Grey

PROPOSED AMENITIES
Construction Certificate Approval Only
316 Springwood Road, Yarramundi NSW 2753
For YMCA Yarramundi

Document Set ID: 8426352
Version: 1, Version Date: 22/05/2023




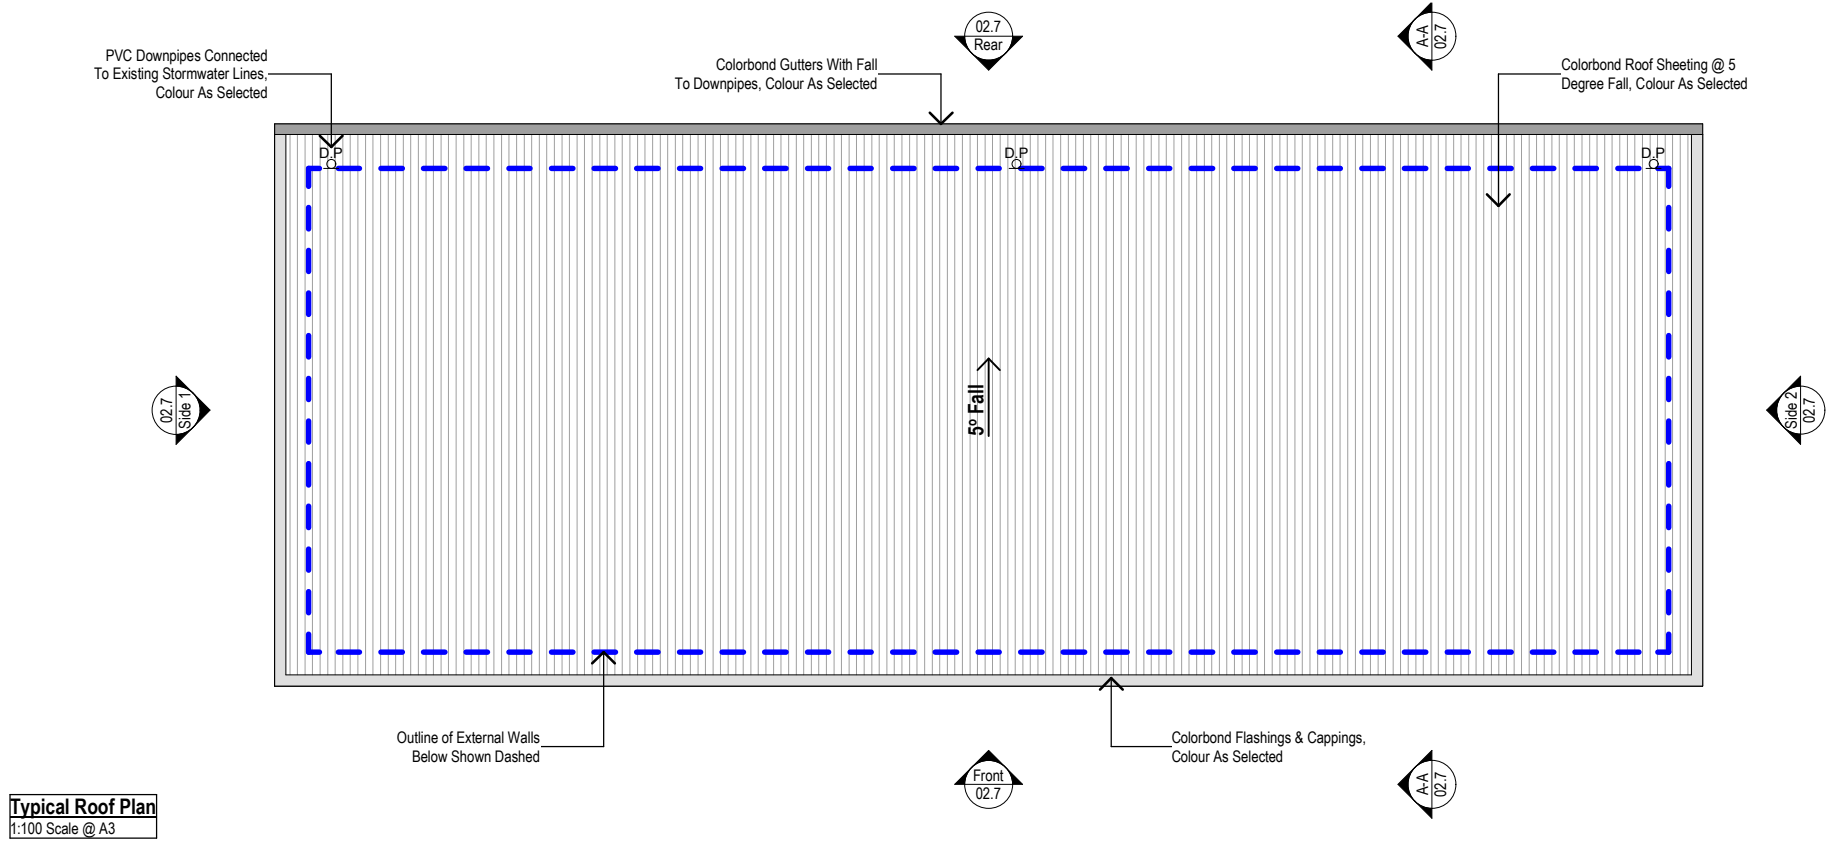
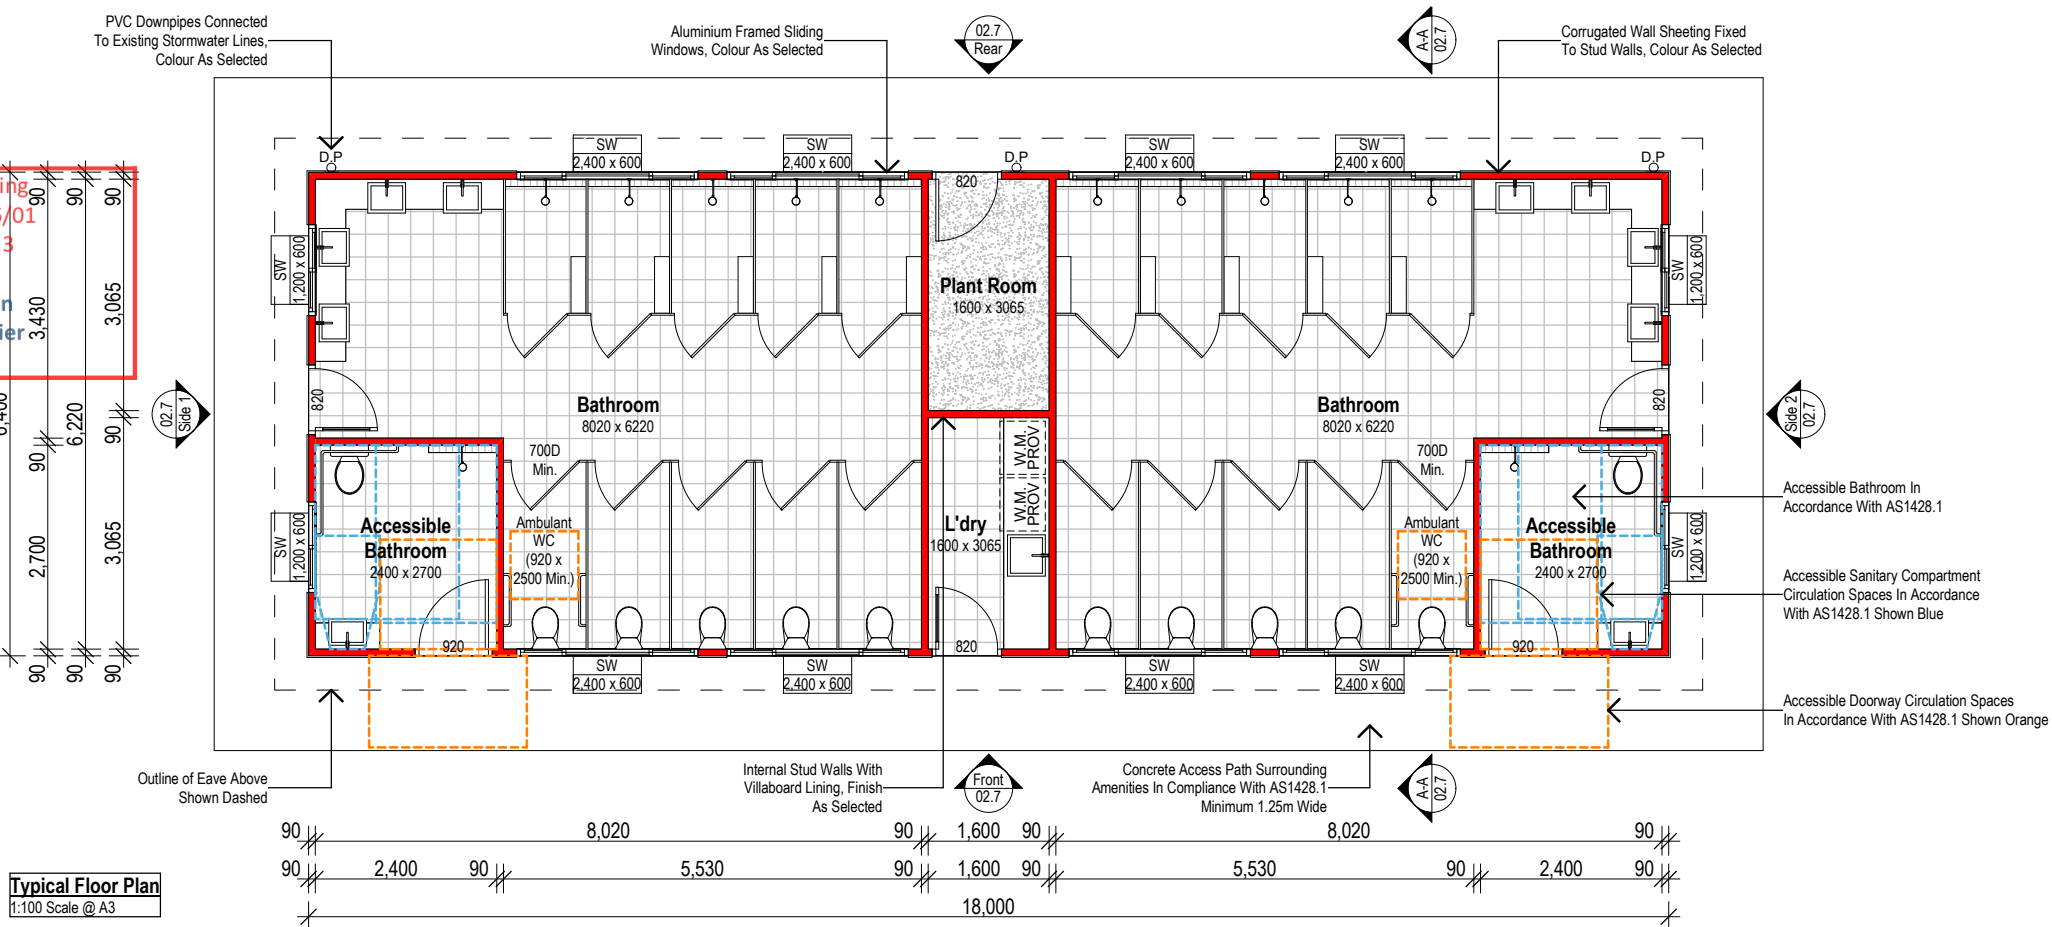


BAL-29 Requirements	
SUBFLOOR SUPPORTS	Enclosure by external wall or by steel, bronze, or aluminium mesh, non-combustible supports where the subfloor is unenclosed, naturally fire resistant timber stumps or posts on /5mm metal stirrups.
FLOORS	Concrete slab on ground, enclosure by external wall, metal mesh as above or flooring less than 400 mm above ground level to be non-combustible, naturally fire resistant timber or protected on the underside with sarking or mineral wool insulation.
EXTERNAL WALLS	Non-combustible material (masonry, brick veneer, mud brick, aerated concrete, concrete), timber framed, steel framed walls sarked on the outside and clad with 6mm fibre cement sheeting or steel sheeting or bushfire resistant timber.
EXTERNAL WINDOWS	Protected by bushfire shutter or completely screened with steel, bronze or aluminium mesh, or 5mm toughened glass with openable portion screened and frame of metal or metal reinforced PVC-U, or bushfire resisting timber and portion within 400 mm of ground level screened.
EXTERNAL DOORS	Protected by bushfire shutter, or screened with steel, bronze or aluminium mesh or non-combustible, or 35 mm solid timber for 400mm above threshold. Metal or bushfire resisting timber framed tight-fitting with weather strips at base.
ROOFS	Non-combustible covering. Roof/wall junction sealed. Openings fitted with non-combustible ember guards. Roof to be fully sarked.
VERANDAHS, DECKS ETC.	Enclosed sub-floor space or non-combustible or bushfire resistant timber supports. Decking to be non-combustible or bushfire-resisting timber.

Pereira Design & Drafting			Typical Floor Plan & Roof Plan		
Mail: PO Box 3023 Grose Vale NSW 2753			Issue	Description	Date
Phone: 0433 458 857			E	Construction Certificate Issue For Approval	14/03/23
Email: lochie_pereira@hotmail.com			D	Development Application Amendment Issue For Approval	16/06/21
Draftsman Lochlan Pereira - Diploma of Building Design			C	Development Application Amendment Issue For Approval	13/05/21
New Dwellings - Alterations & Additions - Extensions - Dual Occupancies - Townhouses - Granny Flats - Secondary Dwellings - Garages - Carports - Swimming Pools - Basix Reports - Council Application Preparation			B	Development Application Issue For Approval	11/03/21
			A	Preliminary Development Application Issue For Client	10/03/21
			Project Number		2165
			Print Date		Tuesday, 14 March 2023
			Drawn By		Lochlan Pereira
			Scale		1 : 100 @ A3

CC 02.6

Note:
Refer To Site Plan For Amenities
Building Finished Floor Levels

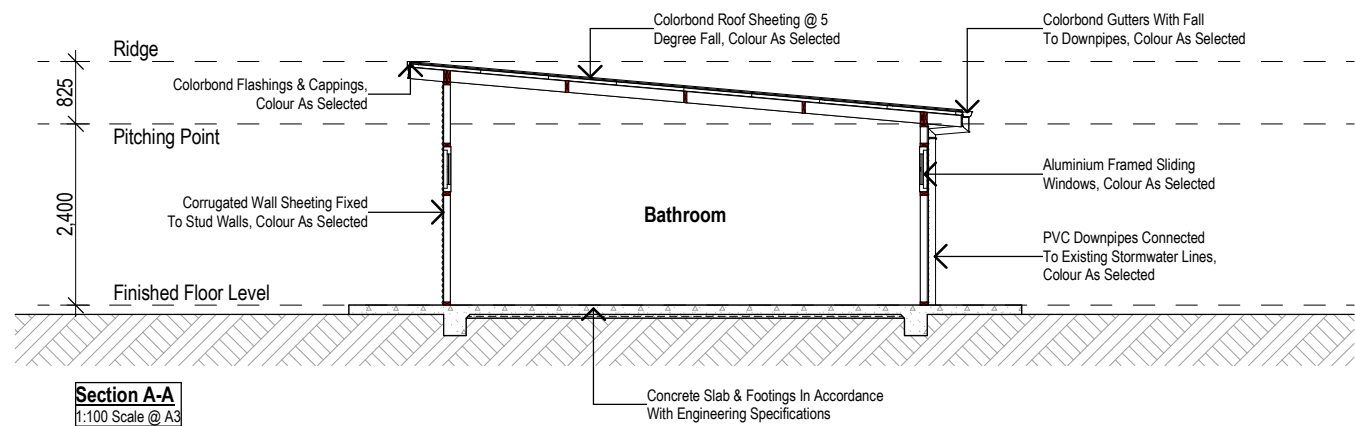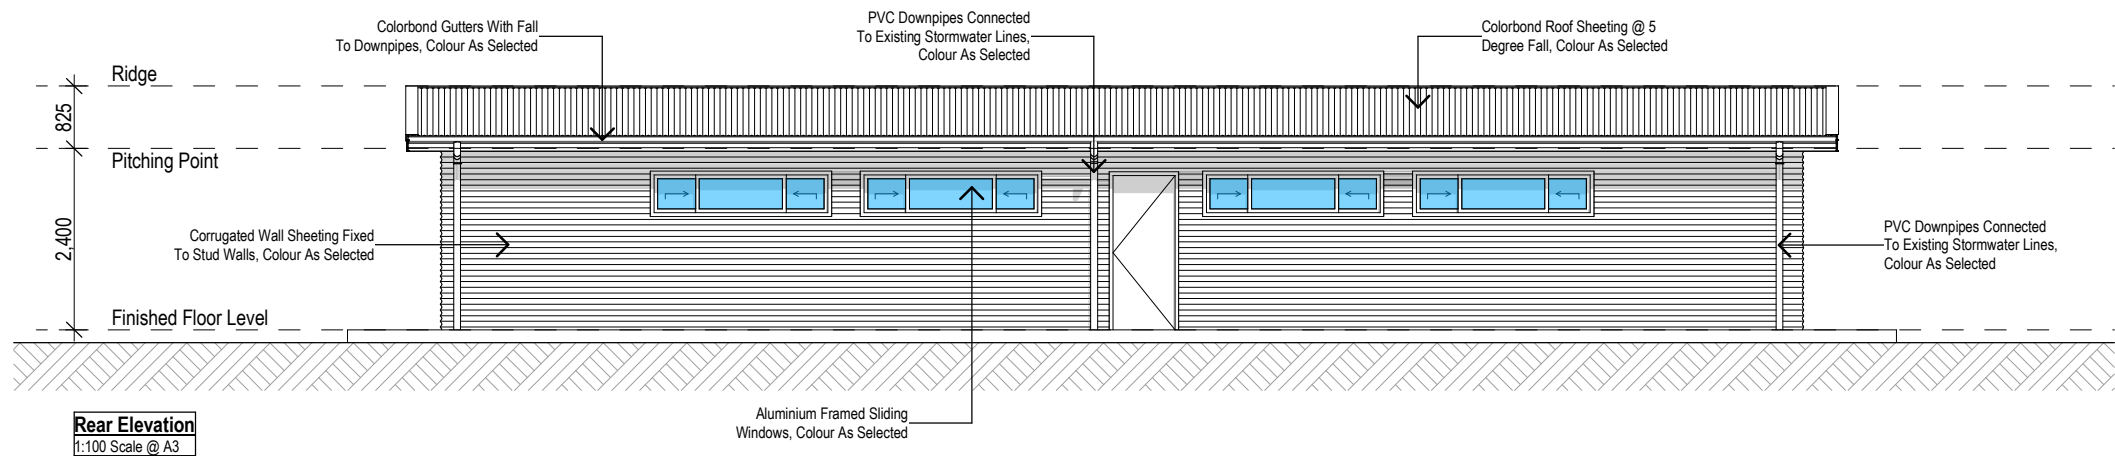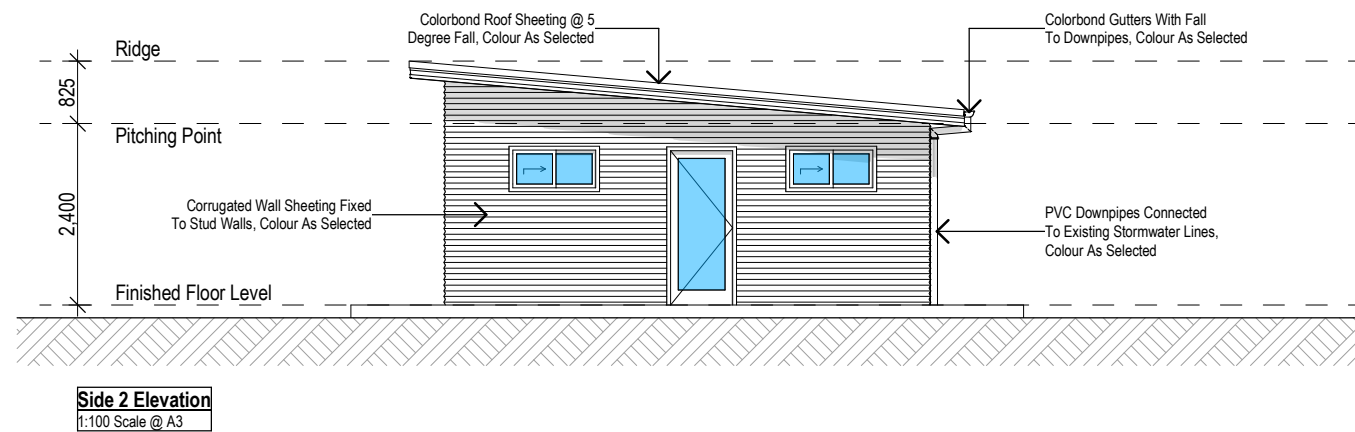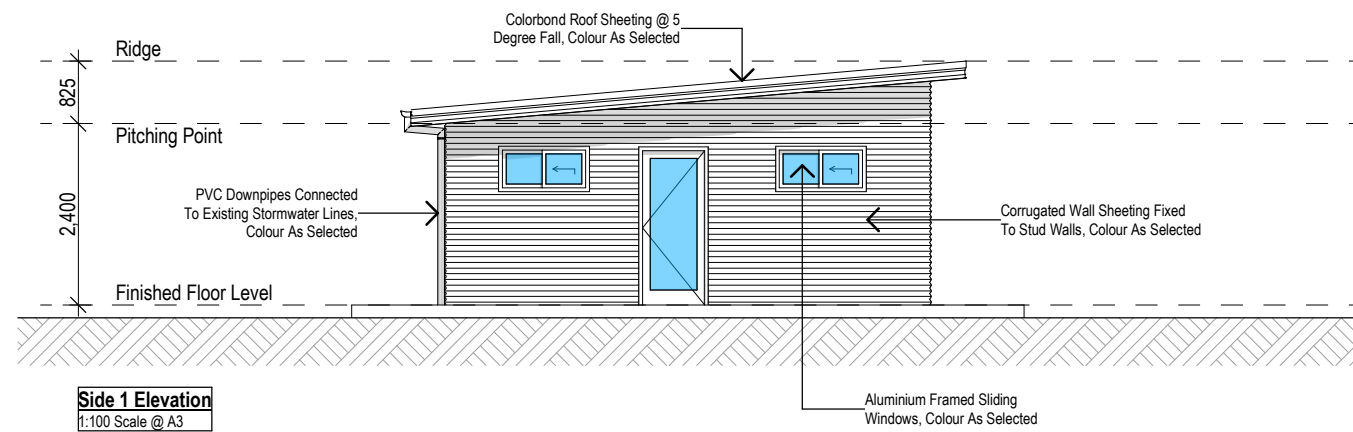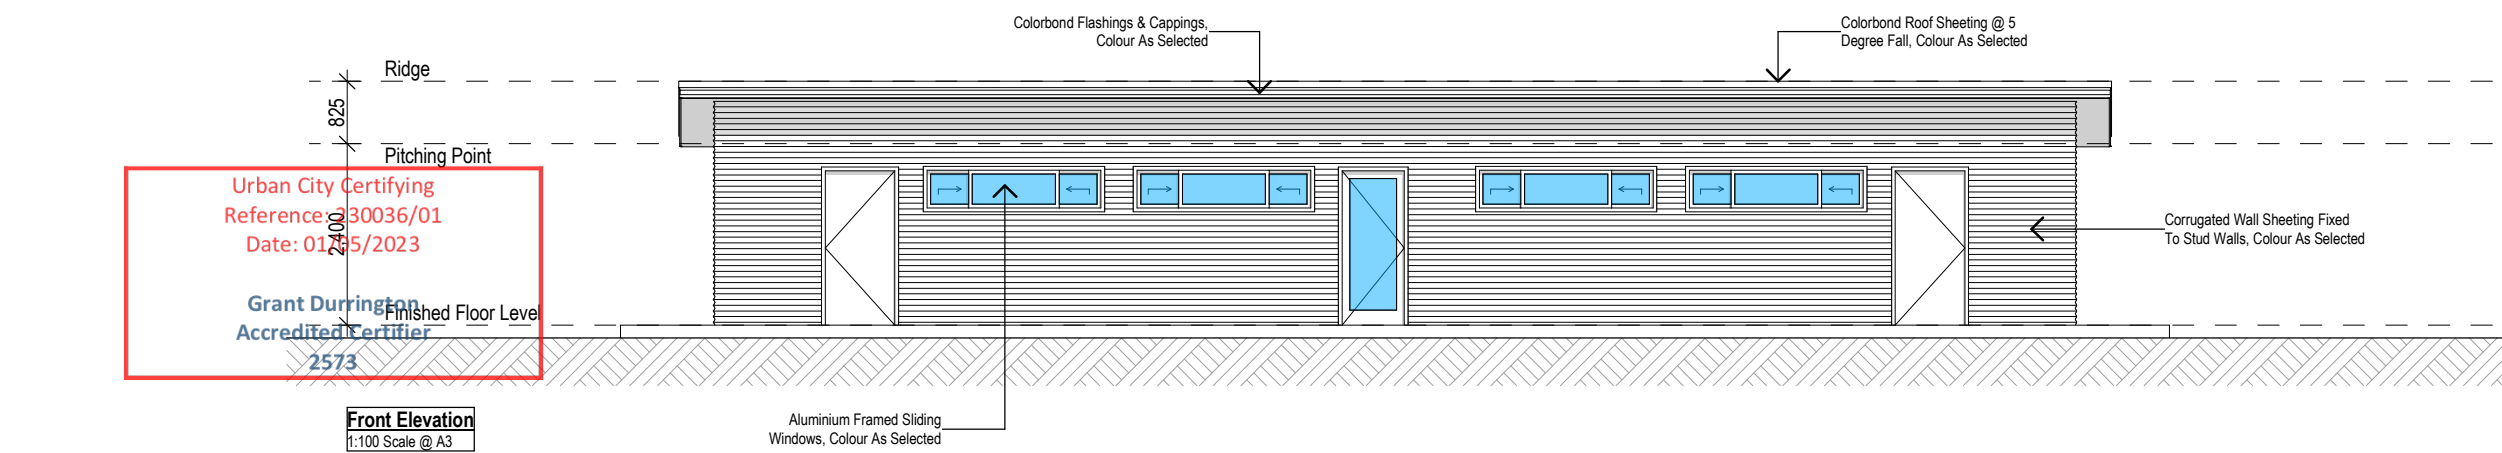

BAL-29 Requirements	
SUBFLOOR SUPPORTS	Enclosure by external wall or by steel, bronze, or aluminium mesh, non-combustible supports where the subfloor is unenclosed, naturally fire resistant timber stumps or posts on 75mm metal stirrups.
FLOORS	Concrete slab on ground, enclosure by external wall, metal mesh as above or flooring less than 400 mm above ground level to be non-combustible, naturally fire resistant timber or protected on the underside with sarking or mineral wool insulation.
EXTERNAL WALLS	Non-combustible material (masonry, brick veneer, mud brick, aerated concrete, concrete), timber framed, steel framed walls sarked on the outside and clad with 6mm fibre cement sheeting or steel sheeting or bushfire resistant timber.
EXTERNAL WINDOWS	Protected by bushfire shutter or completely screened with steel, bronze or aluminium mesh, or 5mm toughened glass with openable portion screened and frame of metal or metal reinforced PVC-U, or bushfire resisting timber and portion within 400 mm of ground level screened.
EXTERNAL DOORS	Protected by bushfire shutter, or screened with steel, bronze or aluminium mesh or non-combustible, or 35 mm solid timber for 400mm above threshold. Metal or bushfire resisting timber framed tight-fitting with weather strips at base.
ROOFS	Non-combustible covering. Roof/wall junction sealed. Openings fitted with non-combustible ember guards. Roof to be fully sarked.
VERANDAHS, DECKS ETC.	Enclosed sub-floor space or non-combustible or bushfire resistant timber supports. Decking to be non-combustible or bushfire-resisting timber.

External Colours:
- Wall Sheetting = Shale Grey
- Windows = Shale Grey
- Downpipes = Shale Grey
- Roof Sheetting/Gutters/Flashings = Woodland Grey

PROPOSED AMENITIES

Construction Certificate Approval Only

316 Springwood Road, Yarramundi NSW 2753

For YMCA Yarramundi

Pereira Design & Drafting

Mail: PO Box 3023 Grose Vale NSW 2753

Phone: 0433 458 857

Email: lochie_pereira@hotmail.com

Draftsman Lochlan Pereira - Diploma of Building Design

New Dwellings - Alterations & Additions - Extensions - Dual Occupancies -

Townhouses - Granny Flats - Secondary Dwellings - Garages -

Carports - Swimming Pools - Basix Reports - Council Application Preparation

Issue	Description	Date	Typical Elevations/Sections	
E	Construction Certificate Issue For Approval	14/03/23	Project Number2165 Print DateTuesday, 14 March 2023 Drawn ByLochlan Pereira Scale1 : 100 @ A3 CC 02.7	
D	Development Application Amendment Issue For Approval	16/06/21		
C	Development Application Amendment Issue For Approval	13/05/21		
B	Development Application Issue For Approval	11/03/21		
A	Preliminary Development Application Issue For Client	10/03/21		